

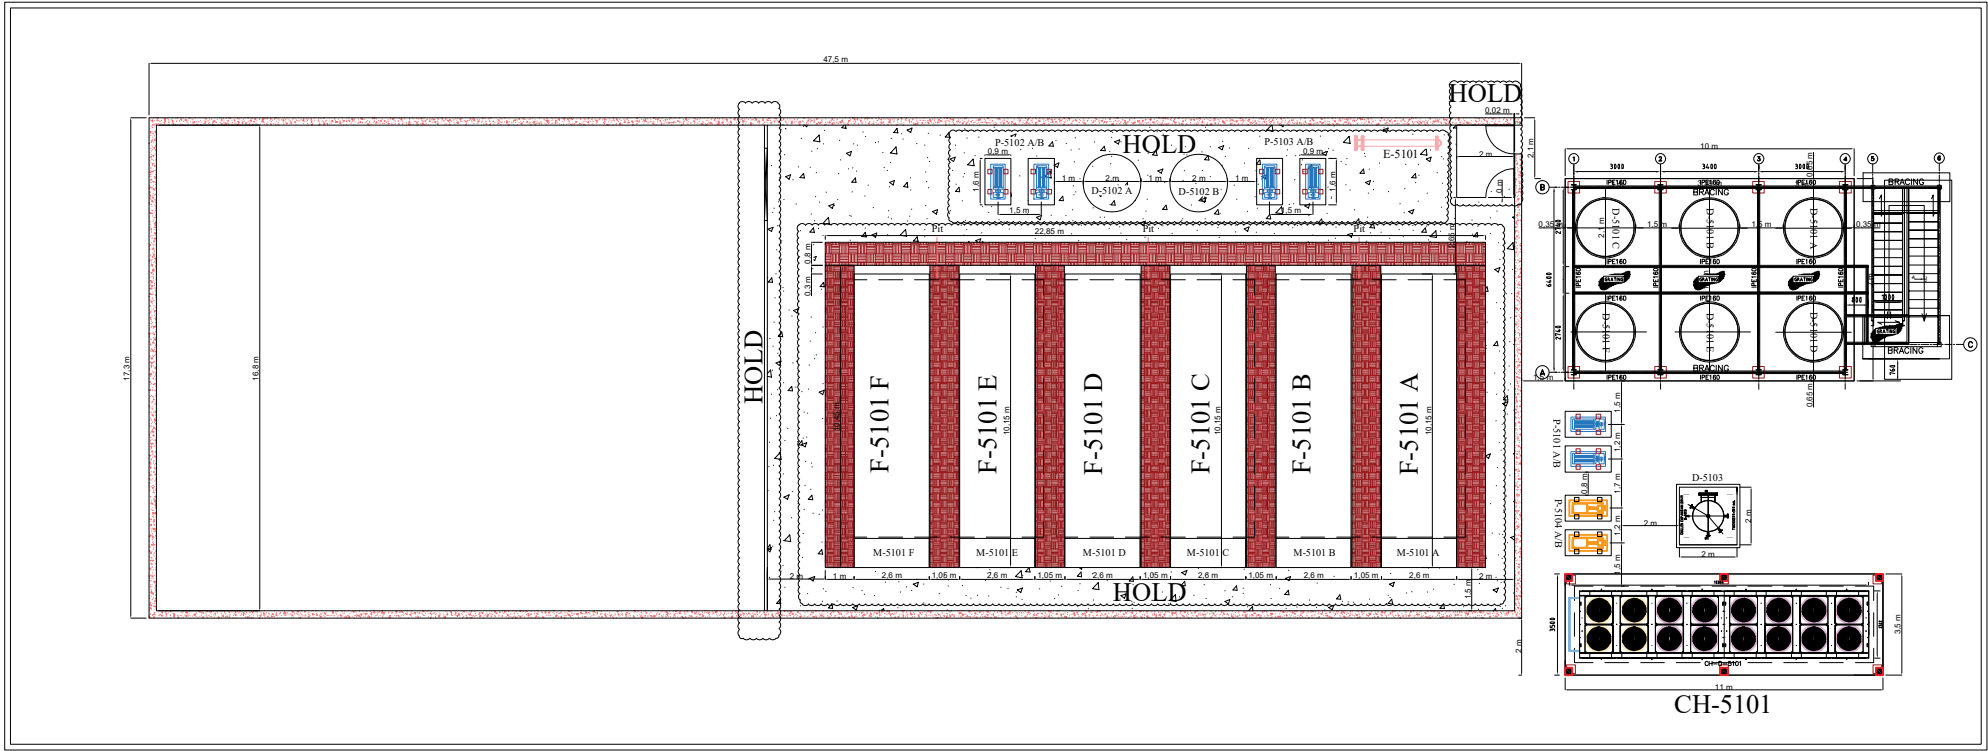


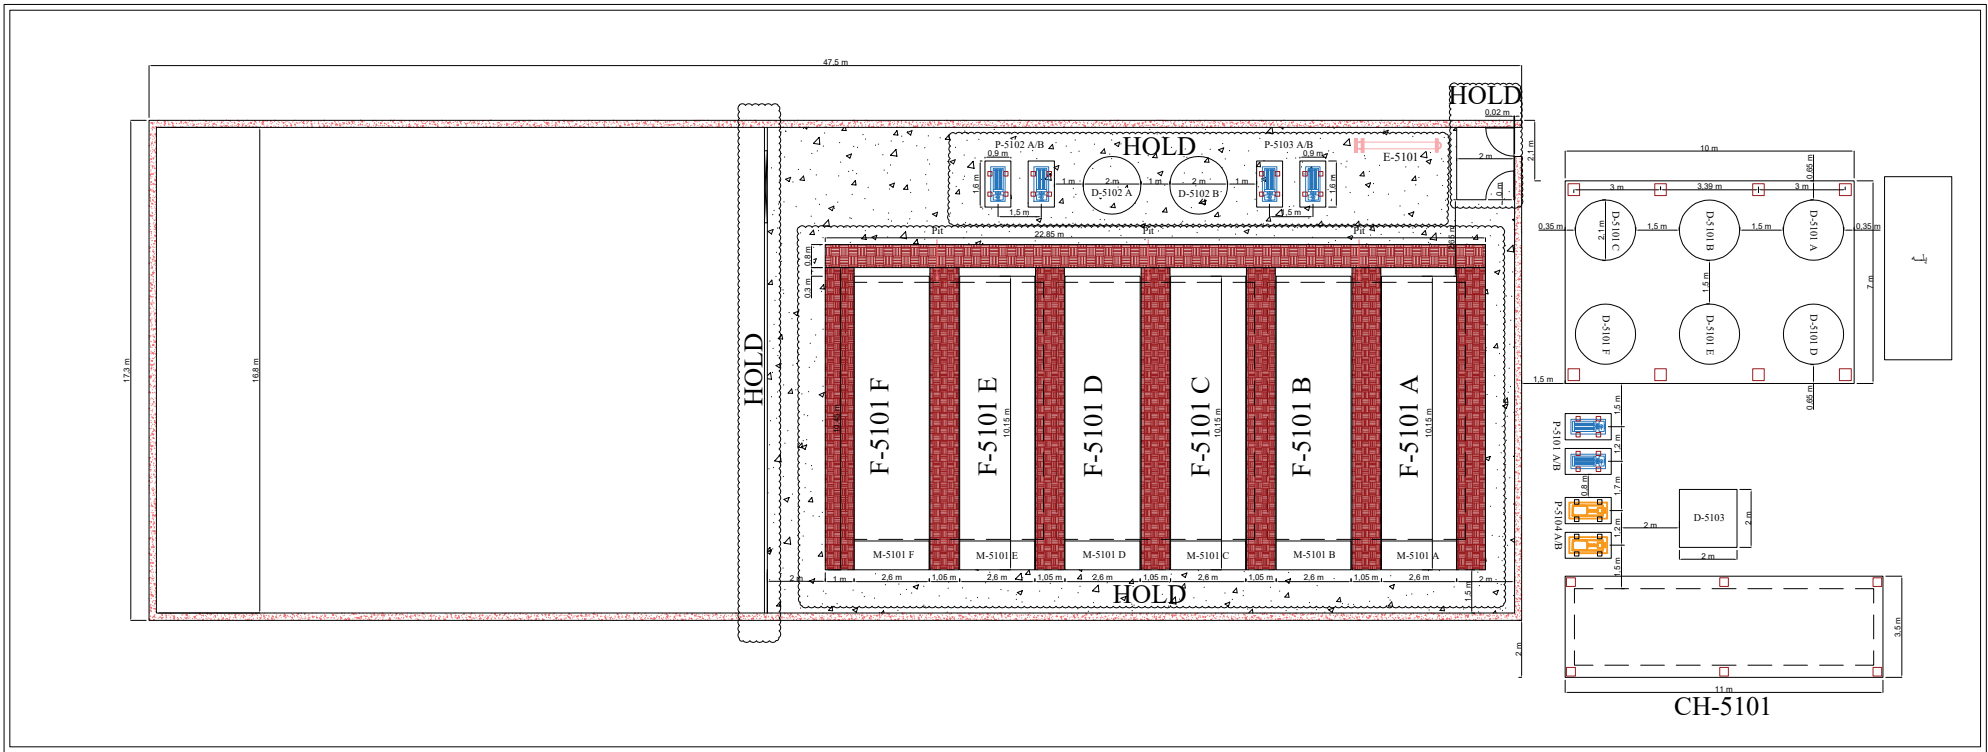

GENERAL NOTE


- 1- ALL DIMENSIONS AND ELEVATIONS ARE IN MILLIMETERS.
2- CONTRACTOR SHOULD CHECK ALL DIMENSION, ELEVATION & COORDINATES BEFOR CONSTRUCTION PHASE.
3- 28 DAY CHARACTERISTIC COMPRESSIVE CYLINDER STRENGTH OF CONCRETE IS 300 Kg/cm2 FOR PITS AND FOUNDATION RESPECTIVELY.
4- 28 DAY CHARACTERISTIC COMPRESSIVE CYLINDER STRENGTH OF CONCRETE IS 150 Kg/cm2 FOR LEAN CONCRETE.
5- THE MATERIAL FOR REINFORCEMENTS SHALL BE ASTM A615 GRADE 60 WITH YIELD STRENGTH GREATER THAN 4000 Kg/cm2.
6- CONCRETE COVER TO REINFORCEMENT SHALL BE 75 mm
7- GRANULAR MATERIAL SHALL BE COMPACTED IN LAYERS NOT EXCEEDING 150 mm TO 95% OF THE MAXIMUM DRY DENSITY AFTER THE CONCRETE ATTAIN THE REQUIRED DESIGN STRENGTH.

- 8- H.P.P.= ---- mm
9-ALL SURFACES OF REINFORCEMENT CONCRETE ITEMS IN DIRECT CONTACT WITH EARTH SHALL BE COATED.
10- PAINTING : ALL BOLT,NUT & WASHER SHALL BE HOT DIP GAL. OR DOCROMET & OTHER PART REFER TO PAITING PROCEDURE.
11-FOR SUPPORT OF FOUNDATION TOP BAR, CHAIR BARS TO BE LOCATED EACH 1.00 m IN BOTH WAYS (IF REQUIRED).
12-MINIMUM CEMENT CONTENT OF CONCRETE SHALL BE 350 Kg/m3.
13-ALL EXPOSED STEEL MEMBERES (GRATING,PLATE & ...) SHALL BE HOT DIP GALVANIZED OR DOCTORATE.
14-FINE SAND WHICH IS LOCATED IN BOTTOM OF TANK SHALL BE WASHED MIN. ONE TIME 15-PORTLAND CEMENT TYPE (II) MUST BE USEDFOR REINFORCED CONCRETE. 16-STRUCTURAL STEEL: ASTM A36 OR EQUIVALENT DIN ST-37 WITH YIELD STRENGTH $F_y=2400$ Kg/Cm2
17-HIGH STRENGTH BOLTS : 2 ASTM A325 TYPE 1 EQUAL TO DIN 8.8 WITH $F_u=8000$ Kg/cm
18-WASHERS ASTM F436
19-WELDING: AWS D1.1 , E70XX ELECTRODE
20-ANCHOR BOLTS: DEFORMED BARS OF ASTM A615 GRADE 60 MINIMUM YIELD STRENGTH $f_y=4000$ Kg/Cm2
21-ALL BOLTED CO
NNECTIONS SHALL BE FULLY TENSIONED FRICTION TYPE CONNECTION.
22-BOLT , NUTS & TREATED PART OF ANCHOR BOLTS SHALL BE DOCROMET.
23- DIMENSIONS "S" OF NON DIMENSIONED FILLET WELDS SHALL AT LEAST BE EQUAL TO 0.7 TIMES THE MINIMUM THICKNESS OF THE SMALLEST ELEMENTS TO BE CONNECTED. MENTIONED WELD USE FOR STIFFENERS, GUSSET PLATE & BUILT-UP H BEAM.

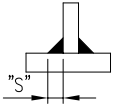

LEGEND

- H.P.P.= HIGHESE POINT OF PAVEMENT
T.O.C.= TOP OF CONCRETE
B.O.F.= BOTTOM OF FOUNDATION
T.O.F.=TOP OF FOUNDATION
T.O.P.= TOP OF PEDESTAL
T.O.WALL.= TOP OF WALL
B.C.D.=BOLT CIRCLE DIAMETER
B.O.L.=BOTTOM OF STABLE GRANULAR LAYER
C.O.SLV.= TOP OF SLEEVE
F.G.L.=FENISH GROUND LEVEL
PED.=PEDESTAL
B.PL.=BASE PLATE
THK=THICKNESS
SWM.=STONE WITH MORTAR

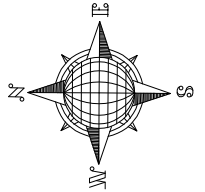



00	08.19.2024	ISSUED FOR CONSTRUCTION	A.D./A.ALI	E.H.	SH.H.
REV.	DATE	DESCRIPTION	PREP./DESI	CHECK	APPR.

CLIENT: Aftab Oil Refining.co


PROJECT : Dewaxing Unit (T05)

TITLE: Plot Plan For Dewaxing Unit

DOC. No.	AOR-VCD-EN-CV-DWG-0000	SIZE	A3
DATE:	08.2024	SHEET 01 OF 10	SCALE: 1:100
REV.	00		

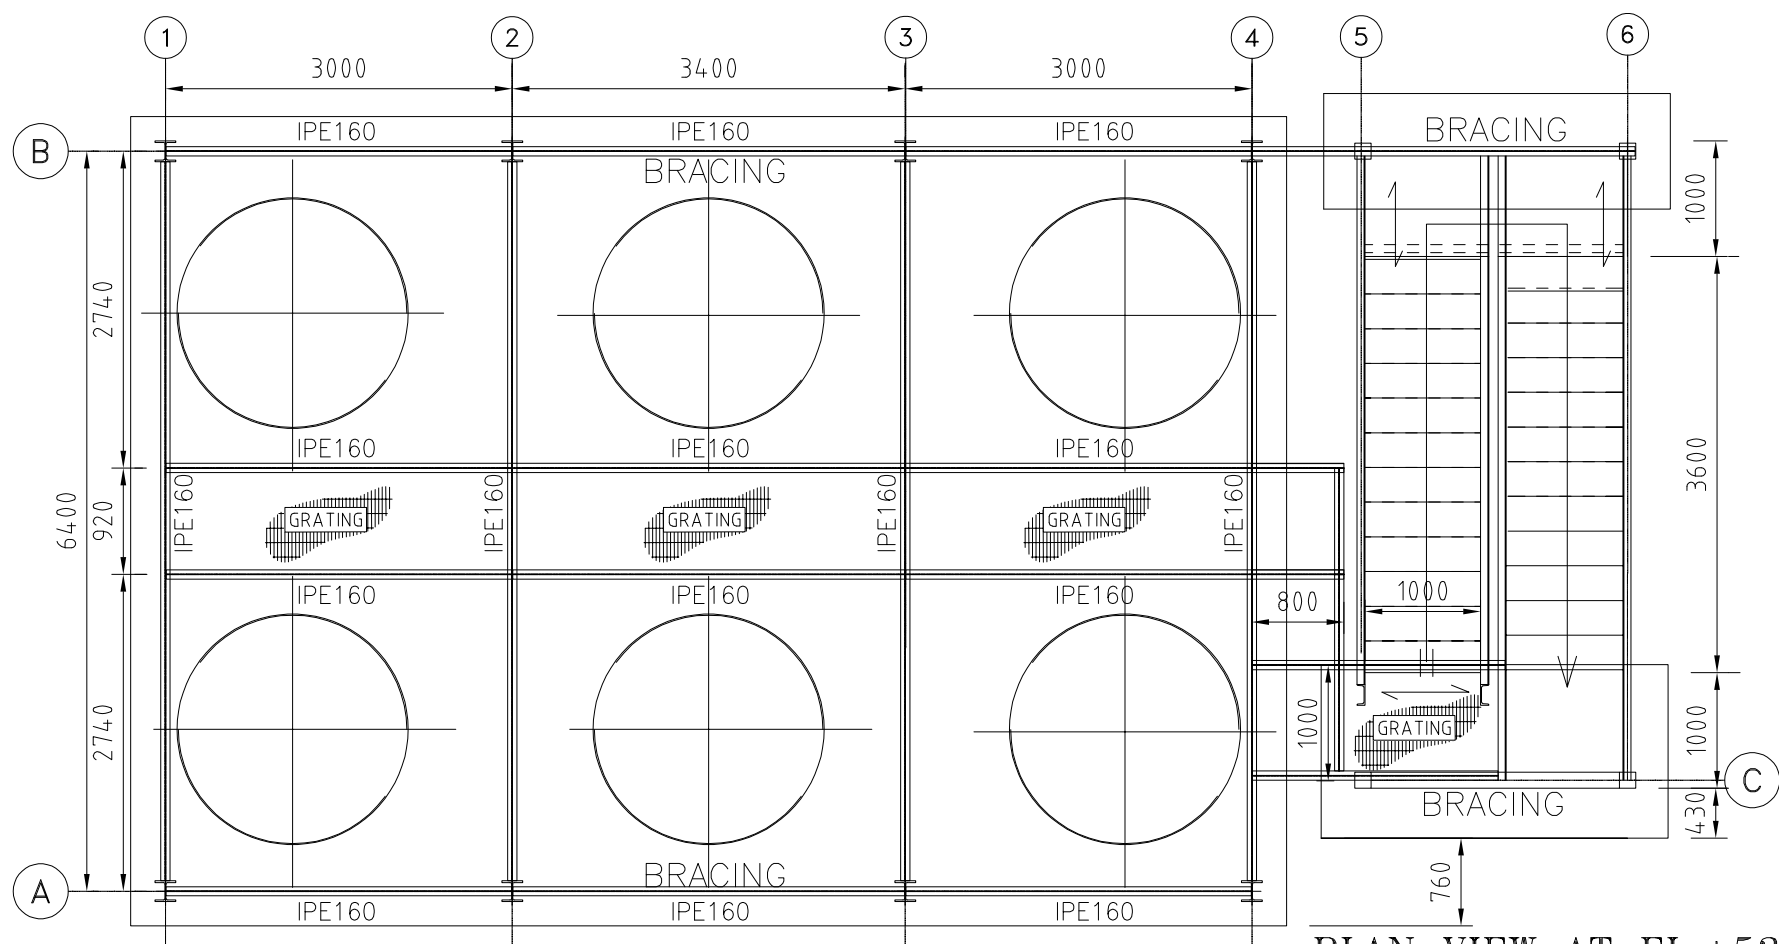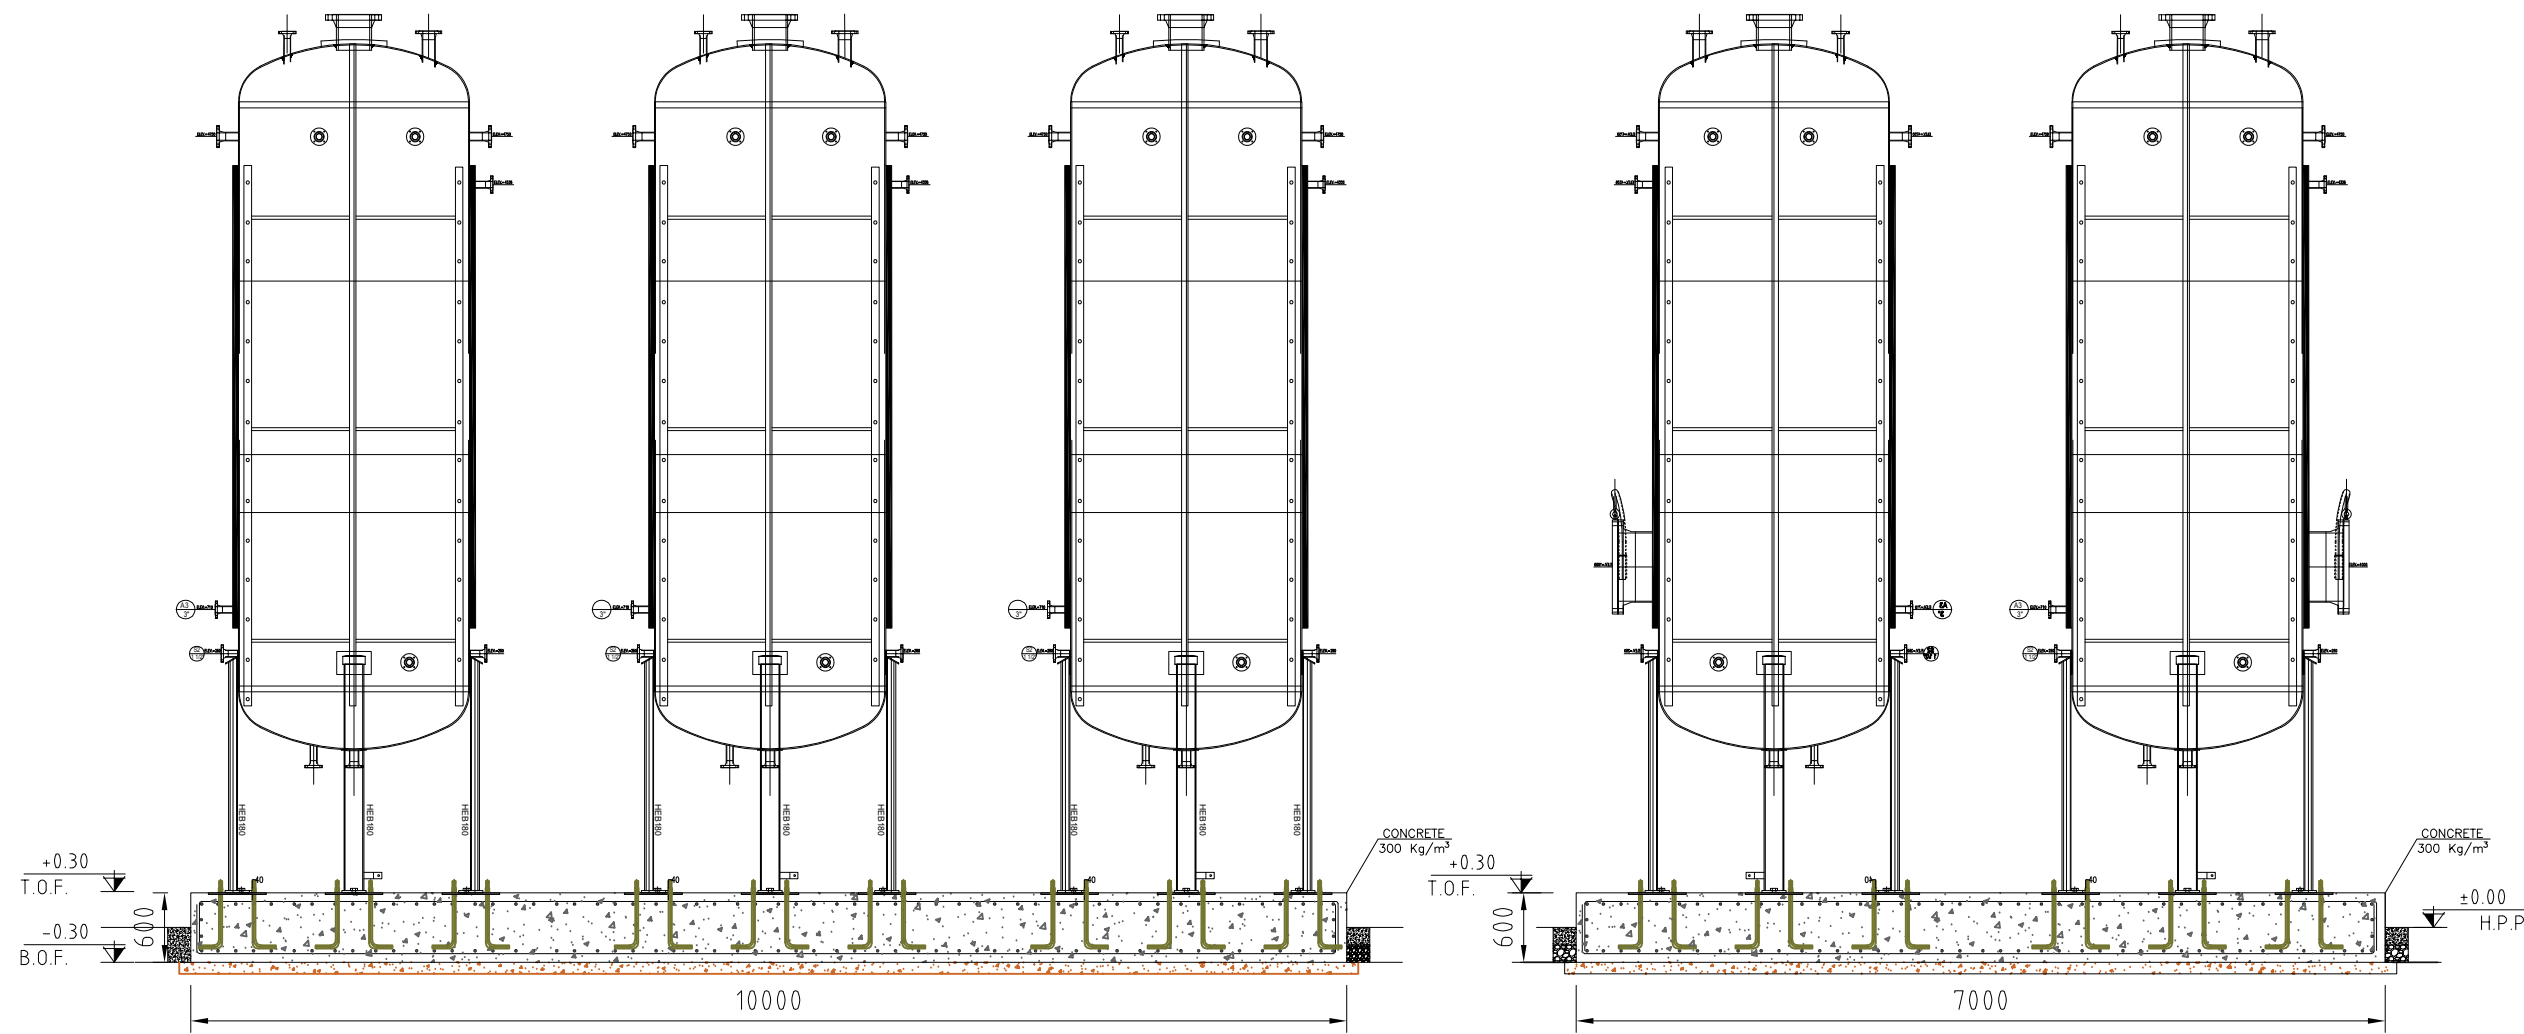


PLAN VIEW AT EL.+5300

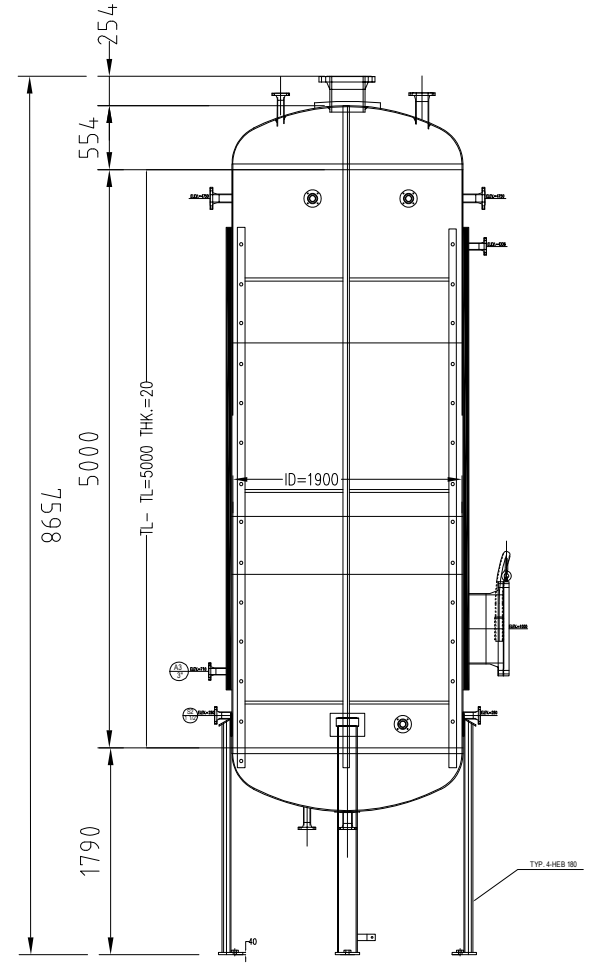


GENERAL NOTE

- 1- ALL DIMENSIONS AND ELEVATIONS ARE IN MILLIMETERS.
- 2- CONTRACTOR SHOULD CHECK ALL DIMENSION, ELEVATION & COORDINATES BEFORE CONSTRUCTION PHASE.
- 3- 28 DAY CHARACTERISTIC COMPRESSIVE CYLINDER STRENGTH OF CONCRETE IS 300 Kg/cm² FOR PITS AND FOUNDATION RESPECTIVELY.
- 4- 28 DAY CHARACTERISTIC COMPRESSIVE CYLINDER STRENGTH OF CONCRETE IS 150 Kg/cm² FOR LEAN CONCRETE.
- 5- THE MATERIAL FOR REINFORCEMENTS SHALL BE ASTM A615 GRADE 60 WITH YIELD STRENGTH GREATER THAN 4000 Kg/cm².
- 6- CONCRETE COVER TO REINFORCEMENT SHALL BE 75 mm
- 7- GRANULAR MATERIAL SHALL BE COMPACTED IN LAYERS NOT EXCEEDING 150 mm TO 95% OF THE MAXIMUM DRY DENSITY AFTER THE CONCRETE ATTAIN THE REQUIRED DESIGN STRENGTH.
- 8- H.P.P.= ----- mm
- 9-ALL SURFACES OF REINFORCEMENT CONCRETE ITEMS IN DIRECT CONTACT WITH EARTH SHALL BE COATED.
- 10- PAINTING : ALL BOLT,NUT & WASHER SHALL BE HOT DIP GAL. OR DOCHROMET & OTHER PART REFER TO PAINTING PROCEDURE.
- 11-FOR SUPPORT OF FOUNDATION TOP BAR, CHAIR BARS TO BE LOCATED EACH 1.00 m IN BOTH WAYS (IF REQUIRED).
- 12-MINIMUM CEMENT CONTENT OF CONCRETE SHALL BE 350 Kg/m³.
- 13-ALL EXPOSED STEEL MEMBERES (GRATING,PLATE & ...) SHALL BE HOT DIP GALVANIZED OR DOCHROMET.
- 14-FINE SAND WHICH IS LOCATED IN BOTTOM OF TANK SHALL BE WASHED MIN. ONE TIME 15-PORTLAND CEMENT TYPE (II) MUST BE USED FOR REINFORCED CONCRETE.
- 16-STRUCTURAL STEEL: ASTM A36 OR EQUIVALENT DIN ST-37 WITH YIELD STRENGTH Fy=2400 Kg/Cm²
- 17-HIGH STRENGTH BOLTS : 2 ASTM A325 TYPE 1 EQUAL TO DIN 8.8 WITH Fu=8000 Kg/cm
- 18-WASHERS ASTM F436
- 19-WELDING: AWS D1.1 , E70XX ELECTRODE
- 20-ANCHOR BOLTS: DEFORMED BARS OF ASTM A615 GRADE 60 MINIMUM YIELD STRENGTH fy=4000 Kg/Cm²
- 21-ALL BOLTED CONNECTIONS SHALL BE FULLY TENSIONED FRICTION TYPE CONNECTION.
- 22-BOLT , NUTS & TREATED PART OF ANCHOR BOLTS SHALL BE DOCHROMET.
- 23- DIMENSIONS "S" OF NON DIMENSIONED FILLET WELDS SHALL AT LEAST BE EQUAL TO 0.7 TIMES THE MINIMUM THICKNESS OF THE SMALLEST ELEMENTS TO BE CONNECTED. MENTIONED WELD USE FOR STIFFENERS, GUSSET PLATE & BUILT-UP H BEAM.

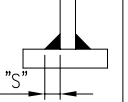

LEGEND

- H.P.P.= HIGHESE POINT OF PAVEMENT
T.O.C.= TOP OF CONCRETE
B.O.F.= BOTTOM OF FOUNDATION
T.O.F.=TOP OF FOUNDATION
T.O.P.= TOP OF PEDESTAL
T.O.WALL.= TOP OF WALL
B.C.D.=BOLT CIRCLE DIAMETER
B.O.L.=BOTTOM OF STABLE GRANULAR LAYER
C.O.SLV.= TOP OF SLEEVE
F.G.L.=FENISH GROUND LEVEL
PED.=PEDESTAL
B.PL.=BASE PLATE
THK=THICKNESS
SWM=STONE WITH MORTAR

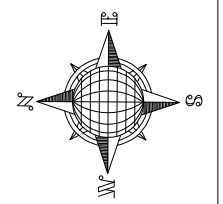

00	08.19.2024	ISSUED FOR CONSTRUCTION	A.D./A.ALI	E.H.	SH.H.
REV.	DATE	DESCRIPTION	PREP./DESI	CHECK	APPR.
CLIENT:					
Aftab Oil Refining.co					
PROJECT :					
Dewaxing Unit (T05)					
TITLE:					
Detail Design Of The Structure For Mixer Iso D-5101 A-F					
DOC. No.	AOR-VCD-EN-CV-DWG-0000	SIZE	A3		
DATE:	08.2024	SHEET 05 OF 10	SCALE: 1:100	REV.	00




M.W.T.	MAX ALLOWABLE WORKING PRESSURE	R.I.	RAIOLIOGRAPHIC TEST
W.P.	WORKING POINT	V.	VAOR
D.P.	DESIGN PRESSURE	P.M.	PLANE NORTH
J.E.	JOINT EFFICIENCY	N.A.	NOT APPLICABLE
L.	LIQUID	B.T.L.	BOTTOM TANGENT LINE
MAT.	MIN. AMBIENT TEMPERATURE	—	—
P.P.	HIGHEST POINT OF PAVING	—	—

1

Aftab Oil Refining.co

DWG. NO.: AOR-DWU-EN-ME-DSH-****		SIZE	A3
DATE : FEB.2023	SHEET 1 OF 1	REV.	00

1		2		3		4		
RevNo	Revision note					Date	Signature	Checked

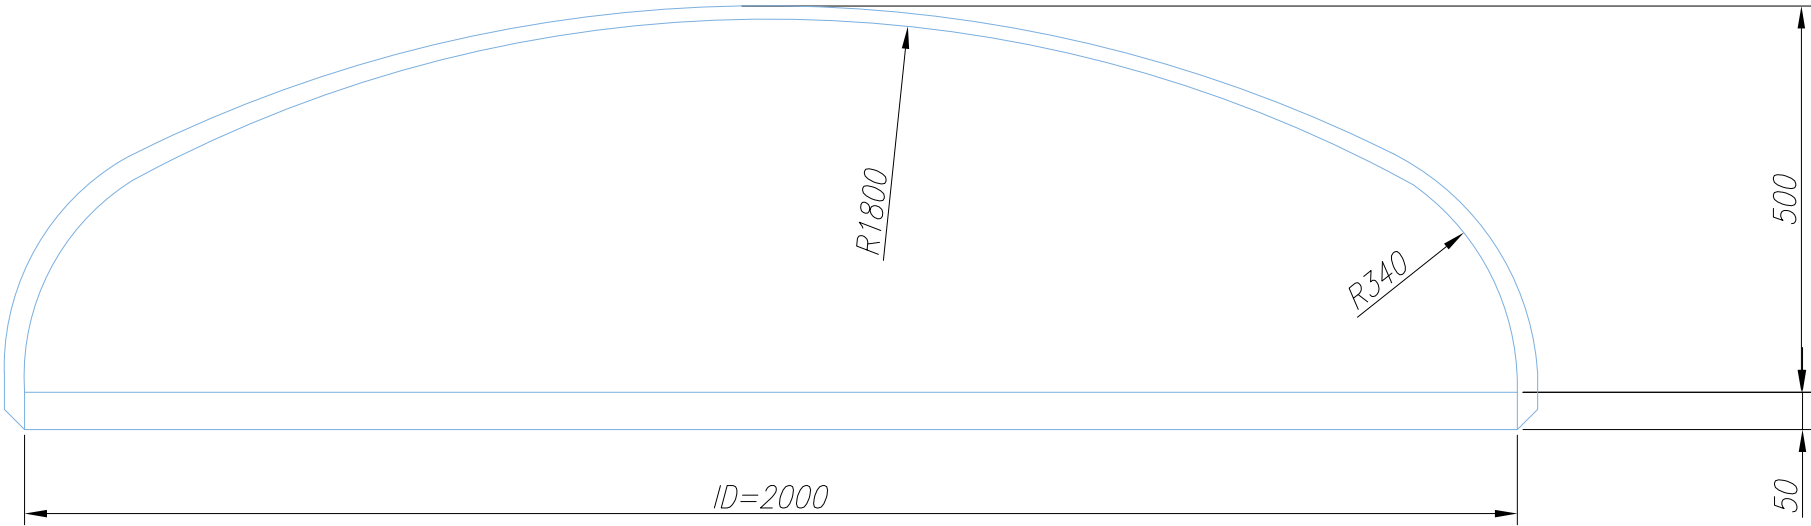

2:1 Elliptical Head ID=2000 mm

MATERIAL: SA-516 GR70

MIN. THK. A.F.=12 mm

QTY.=2

CROWN RADIUS=1800

KNOCKLE RADIUS=340

NOTES:

–ALL DIMENSIONS ARE IN mm.

–DIM. & TOL. STD: ASME SEC. VIII DIV.1

Itemref	Quantity	Title/Name, designation, material, dimension etc			Article No./Reference	
Designed by A.POURKHOSRAVAN		Checked by R.MORADIAN	Approved by SH.HEYDARI	File name	Date	Scale
				CRYSTALLIZER SCRAPER (D-5101A~F)		
						Edition EDITION

6




5

4

3

2

1

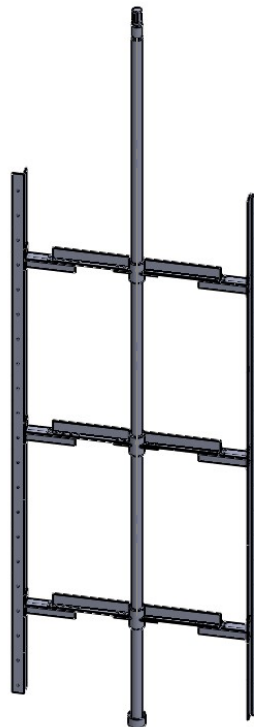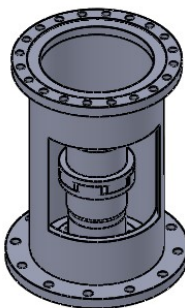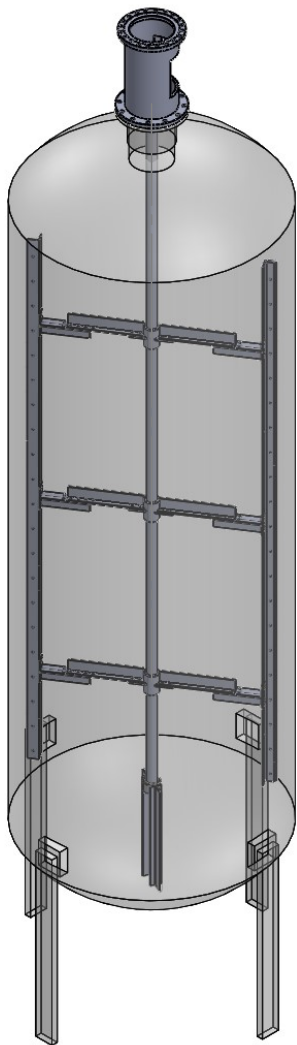

UNLESS OTHERWISE SPECIFIED:
DIMENSIONS ARE IN MILLIMETERS
SURFACE FINISH:
TOLERANCES:
LINEAR:
ANGULAR:

FINISH:

DEBURR AND
BREAK SHARP
EDGES

DO NOT SCALE DRAWING

REVISION

	NAME	SIGNATURE	DATE			
DRAWN						
CHK'D						
APPV'D						
MFG						
Q.A						

TITLE:

MATERIAL:

DWG NO.

...ASEMBLE

A4

WEIGHT:

SCALE:1:100

SHEET 1 OF 1

6

5

4

3

2

1

6



5

4



3

2

1

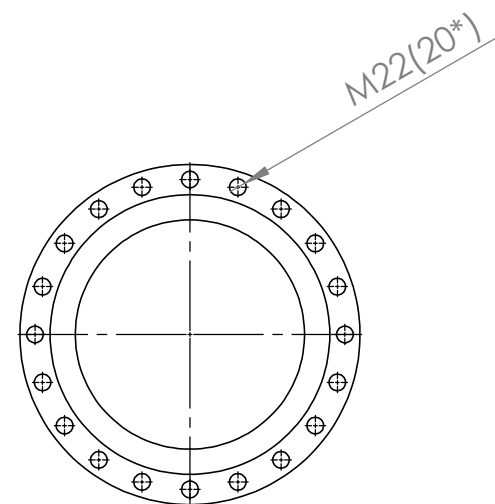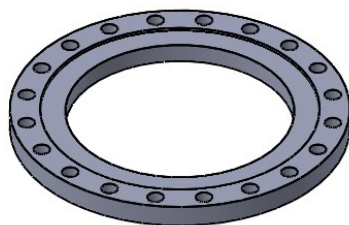

فلنج بالای گلدانی پس از خریداری گیربکس مطابق آن تراشکاری گردد.

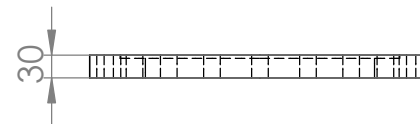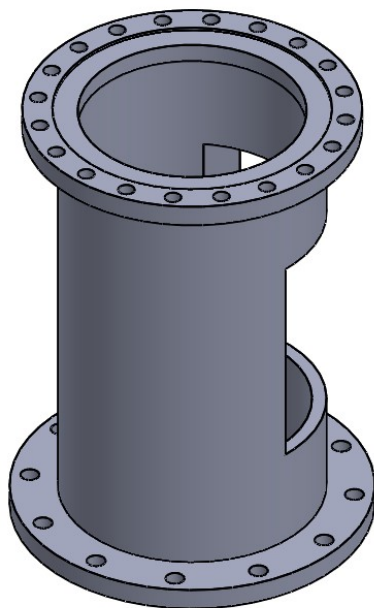

UNLESS OTHERWISE SPECIFIED: DIMENSIONS ARE IN MILLIMETERS SURFACE FINISH: TOLERANCES: LINEAR: ANGULAR:				FINISH:		DEBURR AND BREAK SHARP EDGES		DO NOT SCALE DRAWING		REVISION	
NAME		SIGNATURE		DATE				TITLE:			
DRAWN								UP FLANGE			
CHK'D											
APPV'D											
MFG											
Q.A											
						MATERIAL:		DWG NO.		A4	
								SCALE:1:100		SHEET 1 OF 1	
						WEIGHT:					

6

5

4

3

2

1

6





5

4

3

2

1

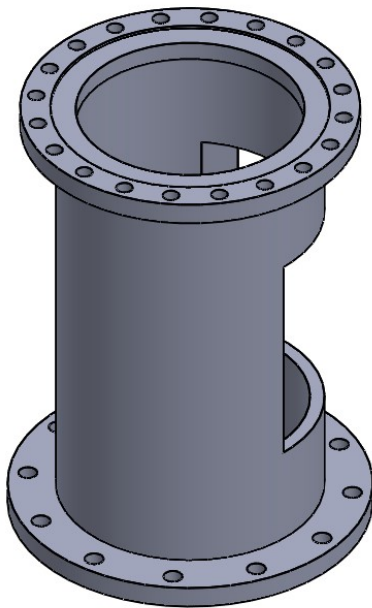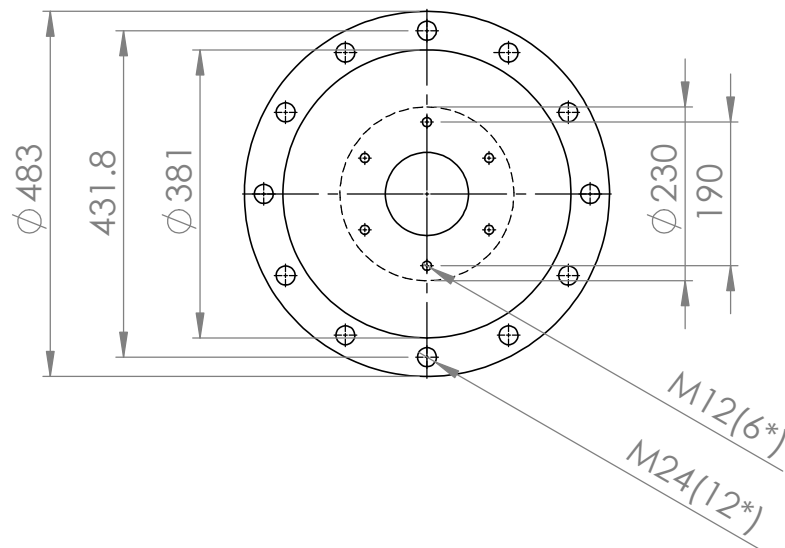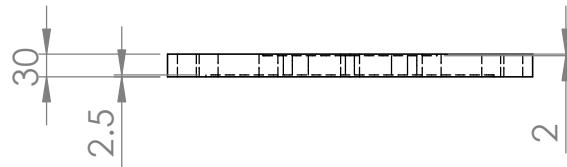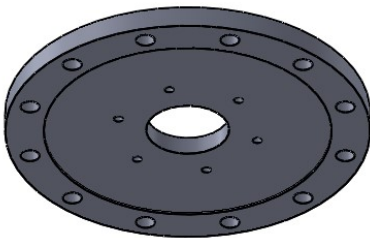

UNLESS OTHERWISE SPECIFIED: DIMENSIONS ARE IN MILLIMETERS SURFACE FINISH: TOLERANCES: LINEAR: ANGULAR:				FINISH:		DEBURR AND BREAK SHARP EDGES		DO NOT SCALE DRAWING		REVISION	
NAME		SIGNATURE		DATE				TITLE:			
DRAWN											
CHK'D											
APPV'D											
MFG											
Q.A											
						MATERIAL:		DWG NO.			
								DOWN FLANGE			
								A4			
						WEIGHT:		SCALE:1:100			
								SHEET 1 OF 1			

6

5

4

3

2

1

6

5





4

3

2

1

پایپ گلدانی پس از خریداری گیربکس مطابق آن تراشکاری گردد.

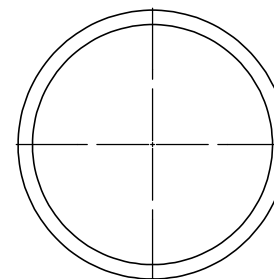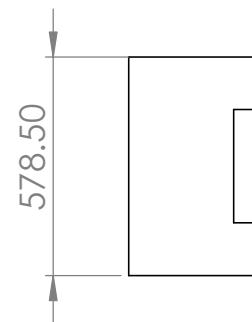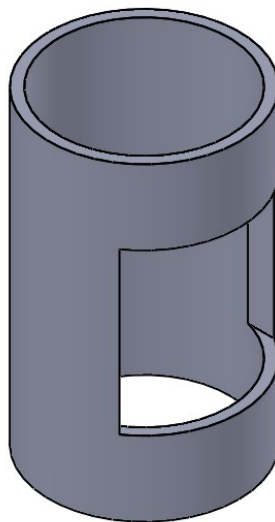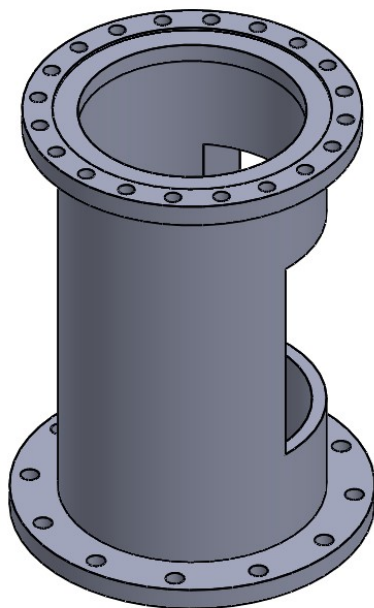

UNLESS OTHERWISE SPECIFIED:
DIMENSIONS ARE IN MILLIMETERS
SURFACE FINISH:
TOLERANCES:
LINEAR:
ANGULAR:

FINISH:

DEBURR AND
BREAK SHARP
EDGES

DO NOT SCALE DRAWING

REVISION

	NAME	SIGNATURE	DATE			
DRAWN						
CHK'D						
APPV'D						
MFG						
Q.A						

TITLE:

MATERIAL:

DWG NO.

PIPE 14"

A4

WEIGHT:

SCALE:1:100

SHEET 1 OF 1

6

5

4

3

2

1

6





5

4

3

2

1

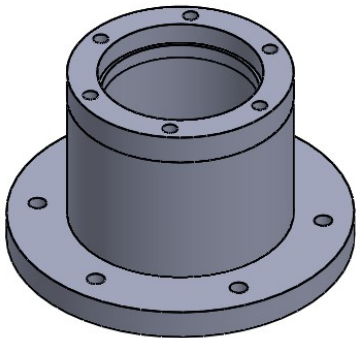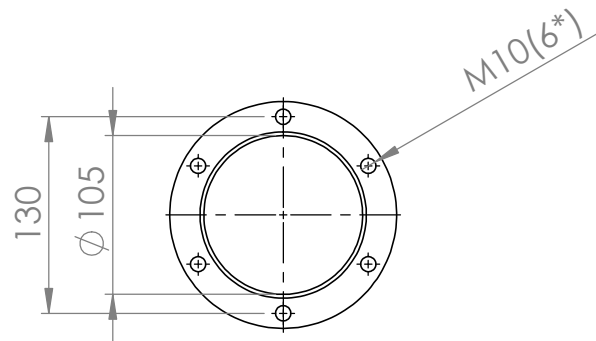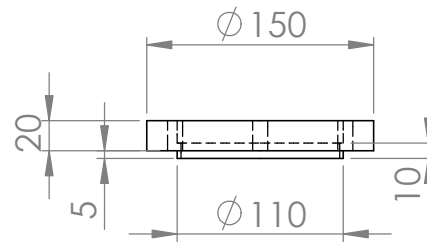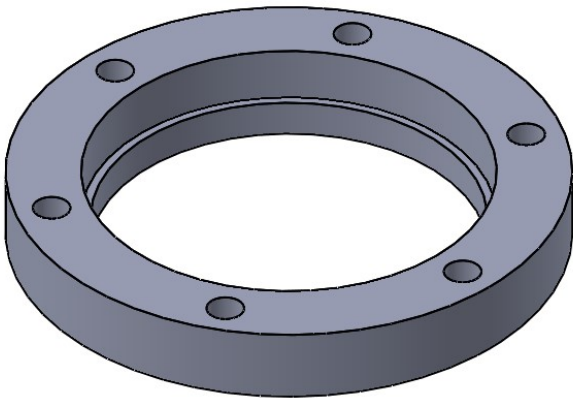

UNLESS OTHERWISE SPECIFIED: DIMENSIONS ARE IN MILLIMETERS SURFACE FINISH: TOLERANCES: LINEAR: ANGULAR:				FINISH:		DEBURR AND BREAK SHARP EDGES		DO NOT SCALE DRAWING		REVISION	
	NAME	SIGNATURE	DATE			TITLE:					
DRAWN											
CHK'D											
APPV'D											
MFG											
Q.A				MATERIAL:		DWG NO. UP HOUSING BEARING					
				WEIGHT:		SCALE:1:100				SHEET 1 OF 1	

A4

6

5

4

3

2

1

6





5

4

3

2

1

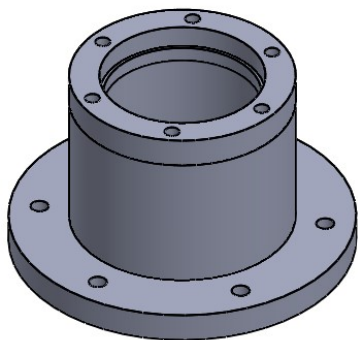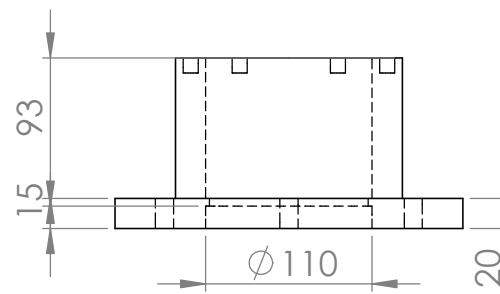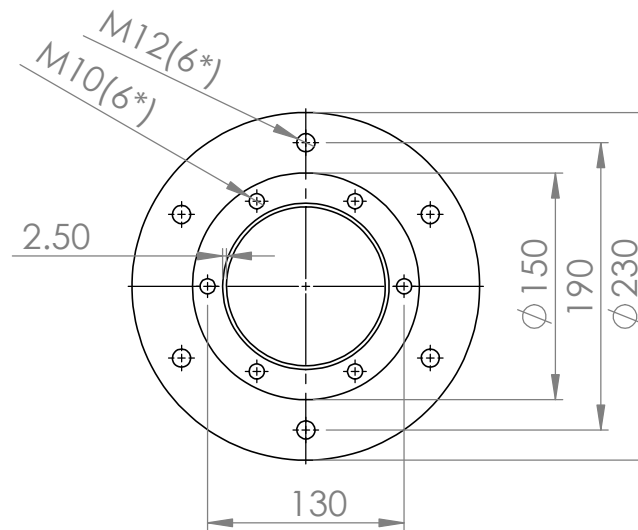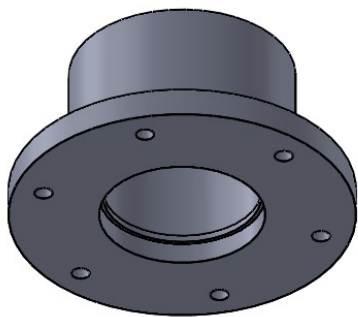

UNLESS OTHERWISE SPECIFIED:
DIMENSIONS ARE IN MILLIMETERS
SURFACE FINISH:
TOLERANCES:
LINEAR:
ANGULAR:

FINISH:

DEBURR AND
BREAK SHARP
EDGES

DO NOT SCALE DRAWING

REVISION

	NAME	SIGNATURE	DATE			
DRAWN						
CHK'D						
APPV'D						
MFG						
Q.A						

TITLE:

DWG NO.

DOWN HOUSING BEARING

A4

WEIGHT:

SCALE:1:100

SHEET 1 OF 1

6

5

4

3

2

1

6



5

4

3

2

1

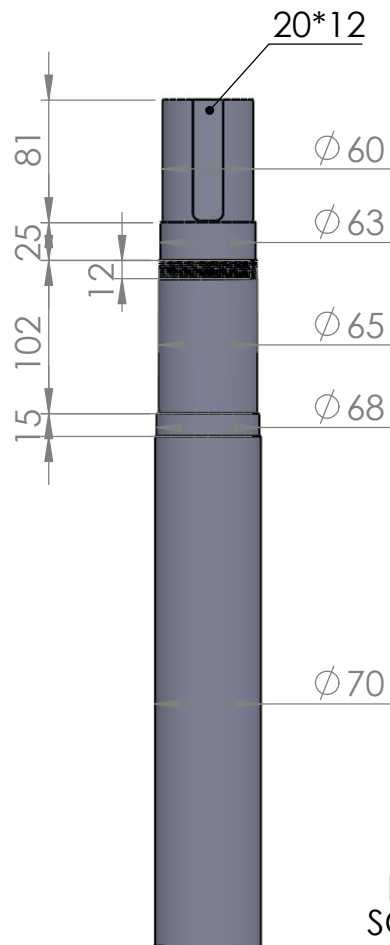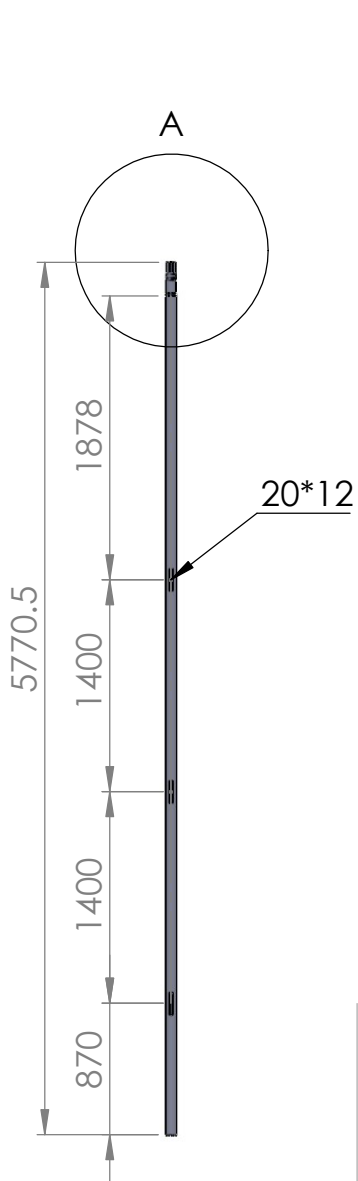

DETAIL A
SCALE 1 : 5

UNLESS OTHERWISE SPECIFIED: DIMENSIONS ARE IN MILLIMETERS SURFACE FINISH: TOLERANCES: LINEAR: ANGULAR:				FINISH:		DEBURR AND BREAK SHARP EDGES		DO NOT SCALE DRAWING		REVISION	
		NAME		SIGNATURE		DATE				TITLE:	
DRAWN											
CHK'D											
APPV'D											
MFG											
Q.A								MATERIAL:		DWG NO.	
										SHAFT	
										A4	
								WEIGHT:		SCALE:1:100	
										SHEET 1 OF 1	

6

5

4

3

2

1

6




5

4

3

2

1

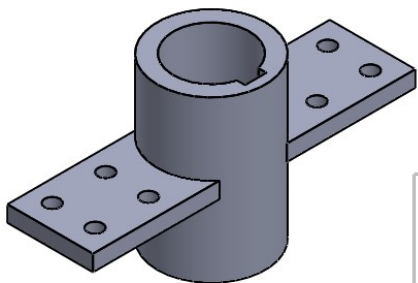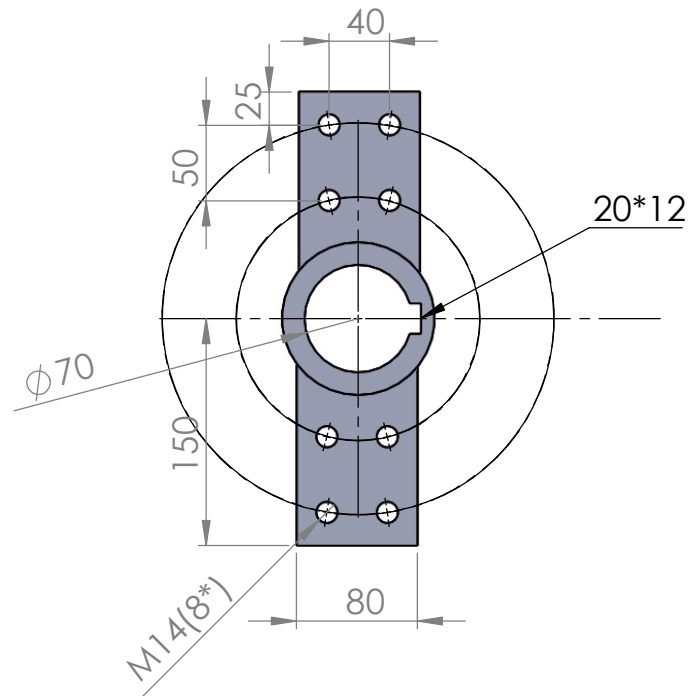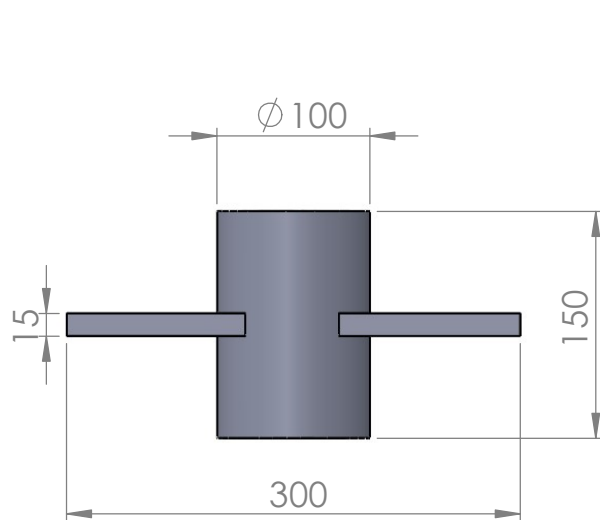

UNLESS OTHERWISE SPECIFIED:
DIMENSIONS ARE IN MILLIMETERS
SURFACE FINISH:
TOLERANCES:
LINEAR:
ANGULAR:

FINISH:

DEBURR AND
BREAK SHARP
EDGES

DO NOT SCALE DRAWING

REVISION

	NAME	SIGNATURE	DATE			
DRAWN						
CHK'D						
APPV'D						
MFG						
Q.A						

TITLE:

MATERIAL:

DWG NO.

HUB

A4

WEIGHT:

SCALE:1:100

SHEET 1 OF 1

6

5

4

3

2

1

6





5

4

3

2

1

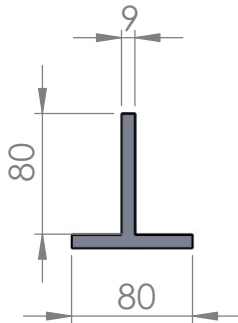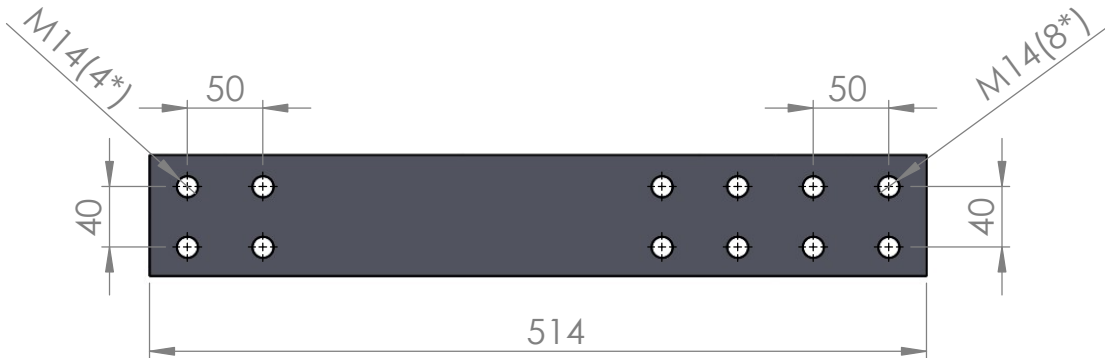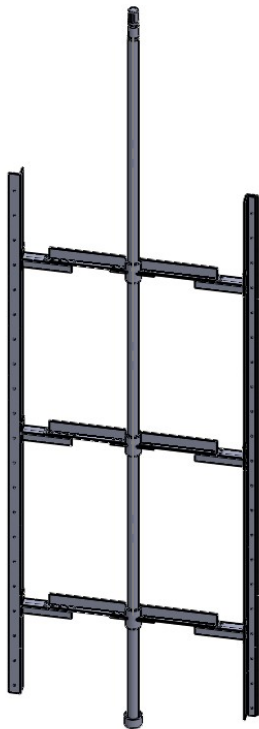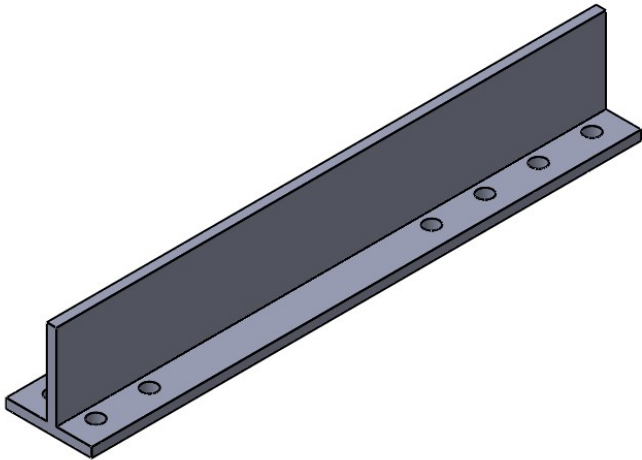

UNLESS OTHERWISE SPECIFIED: DIMENSIONS ARE IN MILLIMETERS SURFACE FINISH: TOLERANCES: LINEAR: ANGULAR:				FINISH:		DEBURR AND BREAK SHARP EDGES		DO NOT SCALE DRAWING		REVISION	
	NAME	SIGNATURE	DATE			TITLE:					
DRAWN											
CHK'D											
APPV'D											
MFG											
Q.A						MATERIAL:		DWG NO.			
								T-PROFILE FIRST			
								A4			
						WEIGHT:		SCALE:1:100			
								SHEET 1 OF 1			

6

5

4

3

2

1

6


5

4




3

2

1

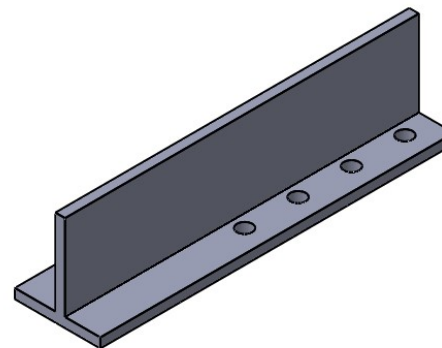

سورخ کاری پس از مونتاژ بازوها اعمال گردد.

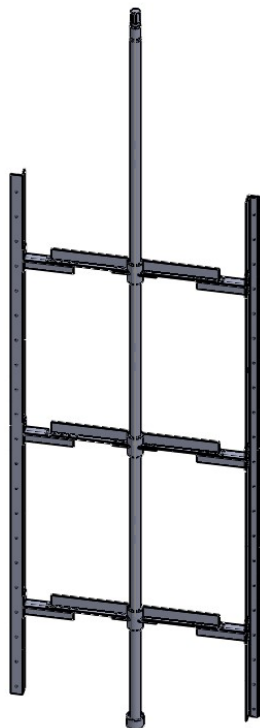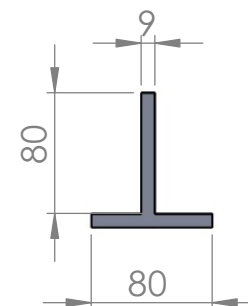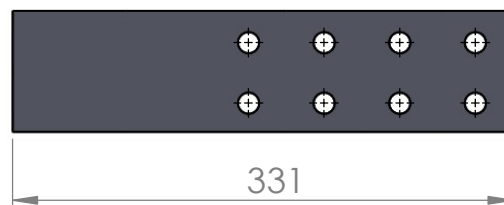

UNLESS OTHERWISE SPECIFIED: DIMENSIONS ARE IN MILLIMETERS SURFACE FINISH: TOLERANCES: LINEAR: ANGULAR:				FINISH:		DEBURR AND BREAK SHARP EDGES		DO NOT SCALE DRAWING		REVISION		
	NAME	SIGNATURE	DATE			TITLE:						
DRAWN												
CHK'D												
APPV'D												
MFG												
Q.A				MATERIAL:		DWG NO.				T-PROFILE SECOND		A4
				WEIGHT:		SCALE:1:100				SHEET 1 OF 1		

6

5

4

3

2

1

6




5

4

3

2

1

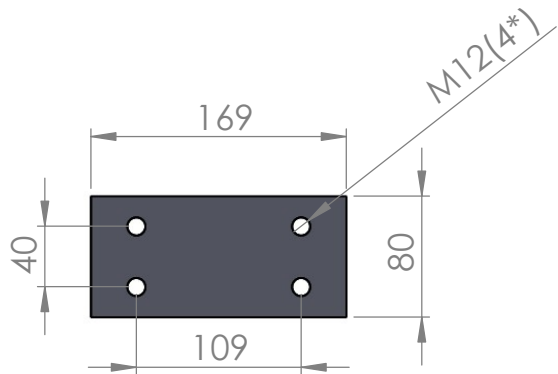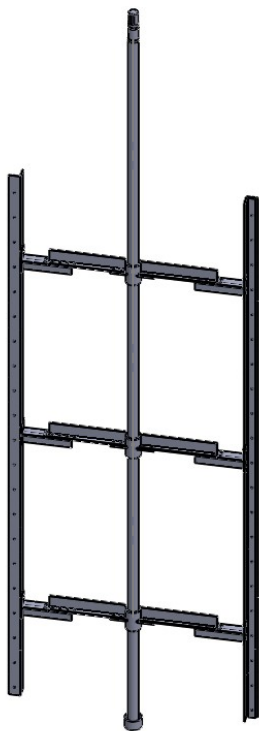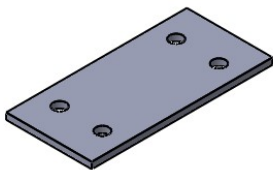

UNLESS OTHERWISE SPECIFIED: DIMENSIONS ARE IN MILLIMETERS SURFACE FINISH: TOLERANCES: LINEAR: ANGULAR:				FINISH:		DEBURR AND BREAK SHARP EDGES		DO NOT SCALE DRAWING		REVISION	
	NAME	SIGNATURE	DATE			TITLE:					
DRAWN											
CHK'D											
APPV'D											
MFG											
Q.A				MATERIAL:		DWG NO. PLATE ANGLE					
				WEIGHT:		SCALE:1:100				SHEET 1 OF 1	

A4

6

5

4

3

2

1

6



5

4

3

2

T

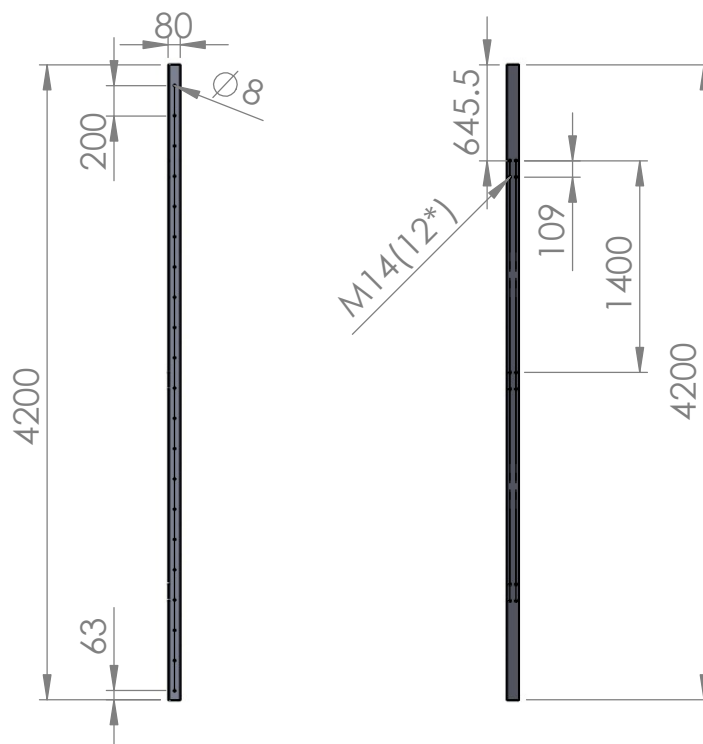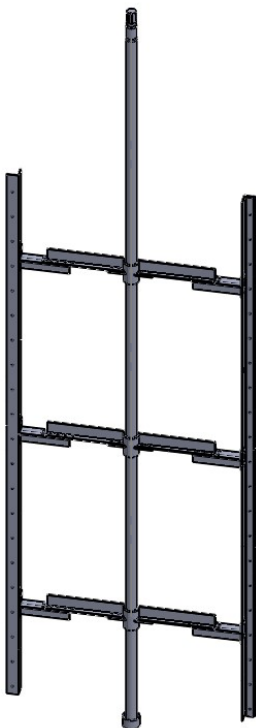

UNLESS OTHERWISE SPECIFIED:
DIMENSIONS ARE IN MILLIMETERS
SURFACE FINISH:
TOLERANCES:
 LINEAR:
 ANGULAR:

FINISH:

DEBURR AND
BREAK SHARP
EDGES

DO NOT SCALE DRAWING

REVISION

DRAWN
CHK'D
APPV'D
MFG
Q.A

NAME _____

SIGNATURE

DATE _____

[illegible]

MATERIAL:

TITLE:

DWG NO.

ANGLE

A4

WEIGHT:

SCALE:1:100

SHEET 1 OF 1

6

5

4

3

2

1

6



5

4

3

2

1

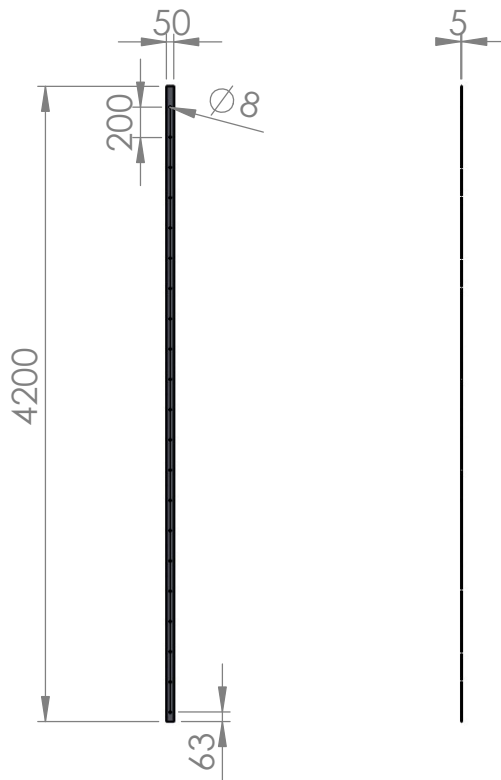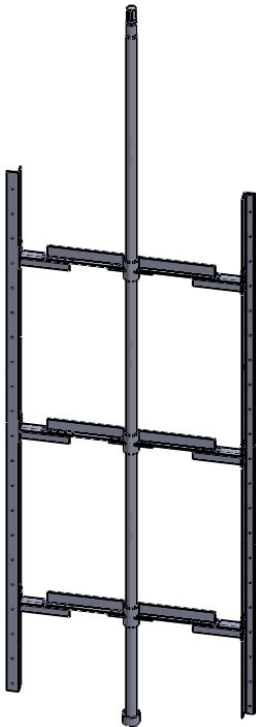

UNLESS OTHERWISE SPECIFIED: DIMENSIONS ARE IN MILLIMETERS SURFACE FINISH: TOLERANCES: LINEAR: ANGULAR:				FINISH:		DEBURR AND BREAK SHARP EDGES		DO NOT SCALE DRAWING		REVISION		
	NAME	SIGNATURE	DATE			TITLE:						
DRAWN												
CHK'D												
APPV'D												
MFG												
Q.A				MATERIAL:		DWG NO.		Flat Bar				A4
				WEIGHT:		SCALE:1:100		SHEET 1 OF 1				

6

5

4

3

2

1

6



5

4

3

2

1

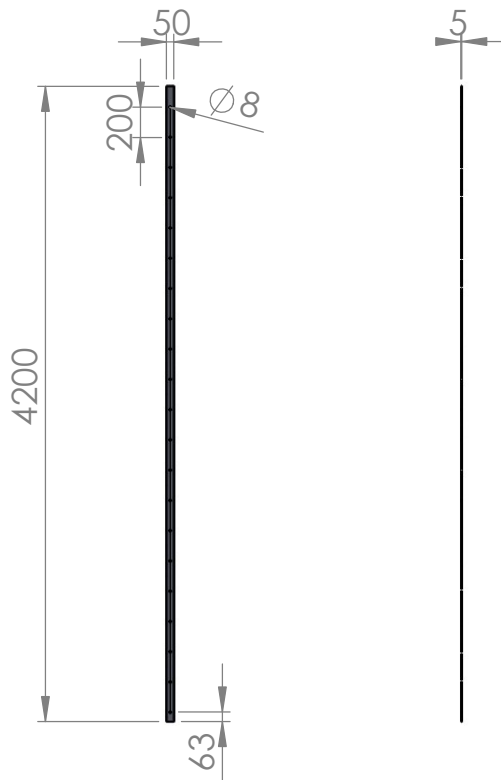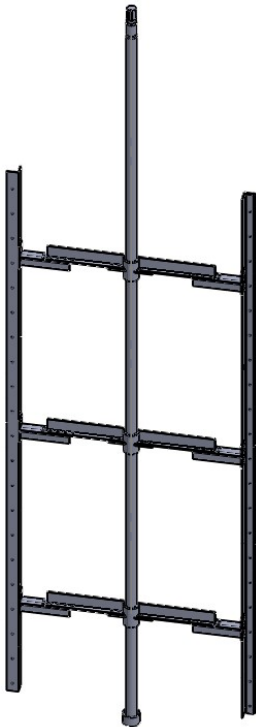

UNLESS OTHERWISE SPECIFIED: DIMENSIONS ARE IN MILLIMETERS SURFACE FINISH: TOLERANCES: LINEAR: ANGULAR:				FINISH:		DEBURR AND BREAK SHARP EDGES		DO NOT SCALE DRAWING		REVISION	
	NAME	SIGNATURE	DATE			TITLE:					
DRAWN											
CHK'D											
APPV'D											
MFG											
Q.A				MATERIAL:		DWG NO. Flat Bar A4					
				WEIGHT:		SCALE:1:100				SHEET 1 OF 1	

6

5

4

3

2

1

6



5

4




3

2



1

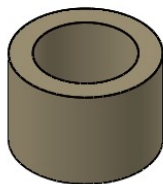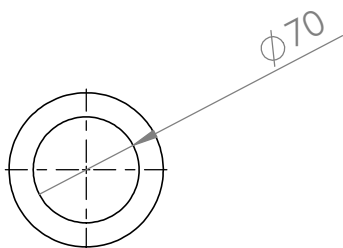

PTFE

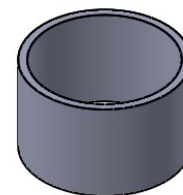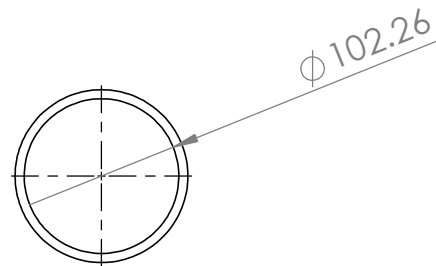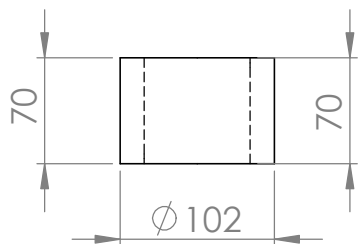

PIPE 4"

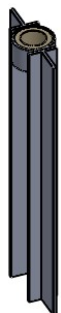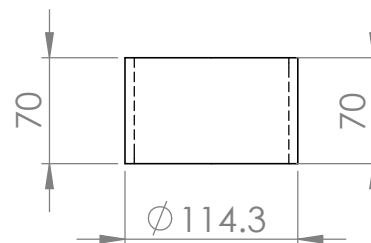

UNLESS OTHERWISE SPECIFIED: DIMENSIONS ARE IN MILLIMETERS SURFACE FINISH: TOLERANCES: LINEAR: ANGULAR:				FINISH:		DEBURR AND BREAK SHARP EDGES		DO NOT SCALE DRAWING		REVISION	
NAME		SIGNATURE		DATE				TITLE:			
DRAWN											
CHK'D											
APPV'D											
MFG											
Q.A						MATERIAL:		DWG NO.			
								PTFE & PIPE4"			
								A4			
						WEIGHT:		SCALE:1:100			
								SHEET 1 OF 1			

6

5

4

3

2

1

6




5

4

3

2

1

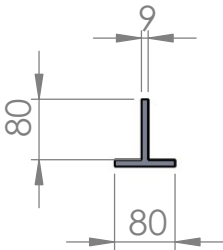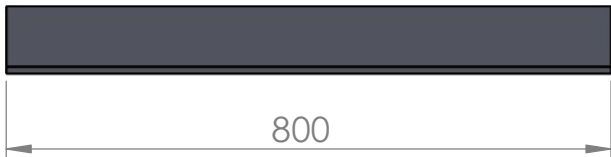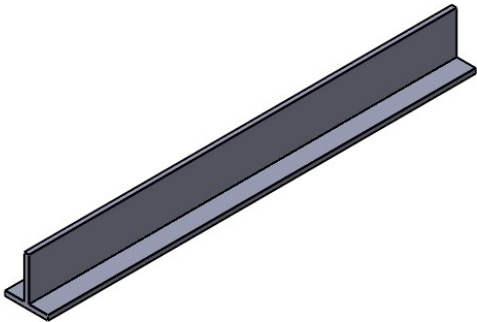

UNLESS OTHERWISE SPECIFIED: DIMENSIONS ARE IN MILLIMETERS SURFACE FINISH: TOLERANCES: LINEAR: ANGULAR:				FINISH:			DEBURR AND BREAK SHARP EDGES		DO NOT SCALE DRAWING		REVISION		
		NAME		SIGNATURE		DATE				TITLE:			
DRAWN													
CHK'D													
APPV'D													
MFG													
Q.A								MATERIAL:		DWG NO.			
										T-PROFILE FIX			
								WEIGHT:		SCALE:1:100			
										SHEET 1 OF 1			

6

5


4

3

2

1

NOTES:
(1) ALL DIMENSIONS ARE IN MILLIMETERS UNLESS OTHERWISE NOTED.

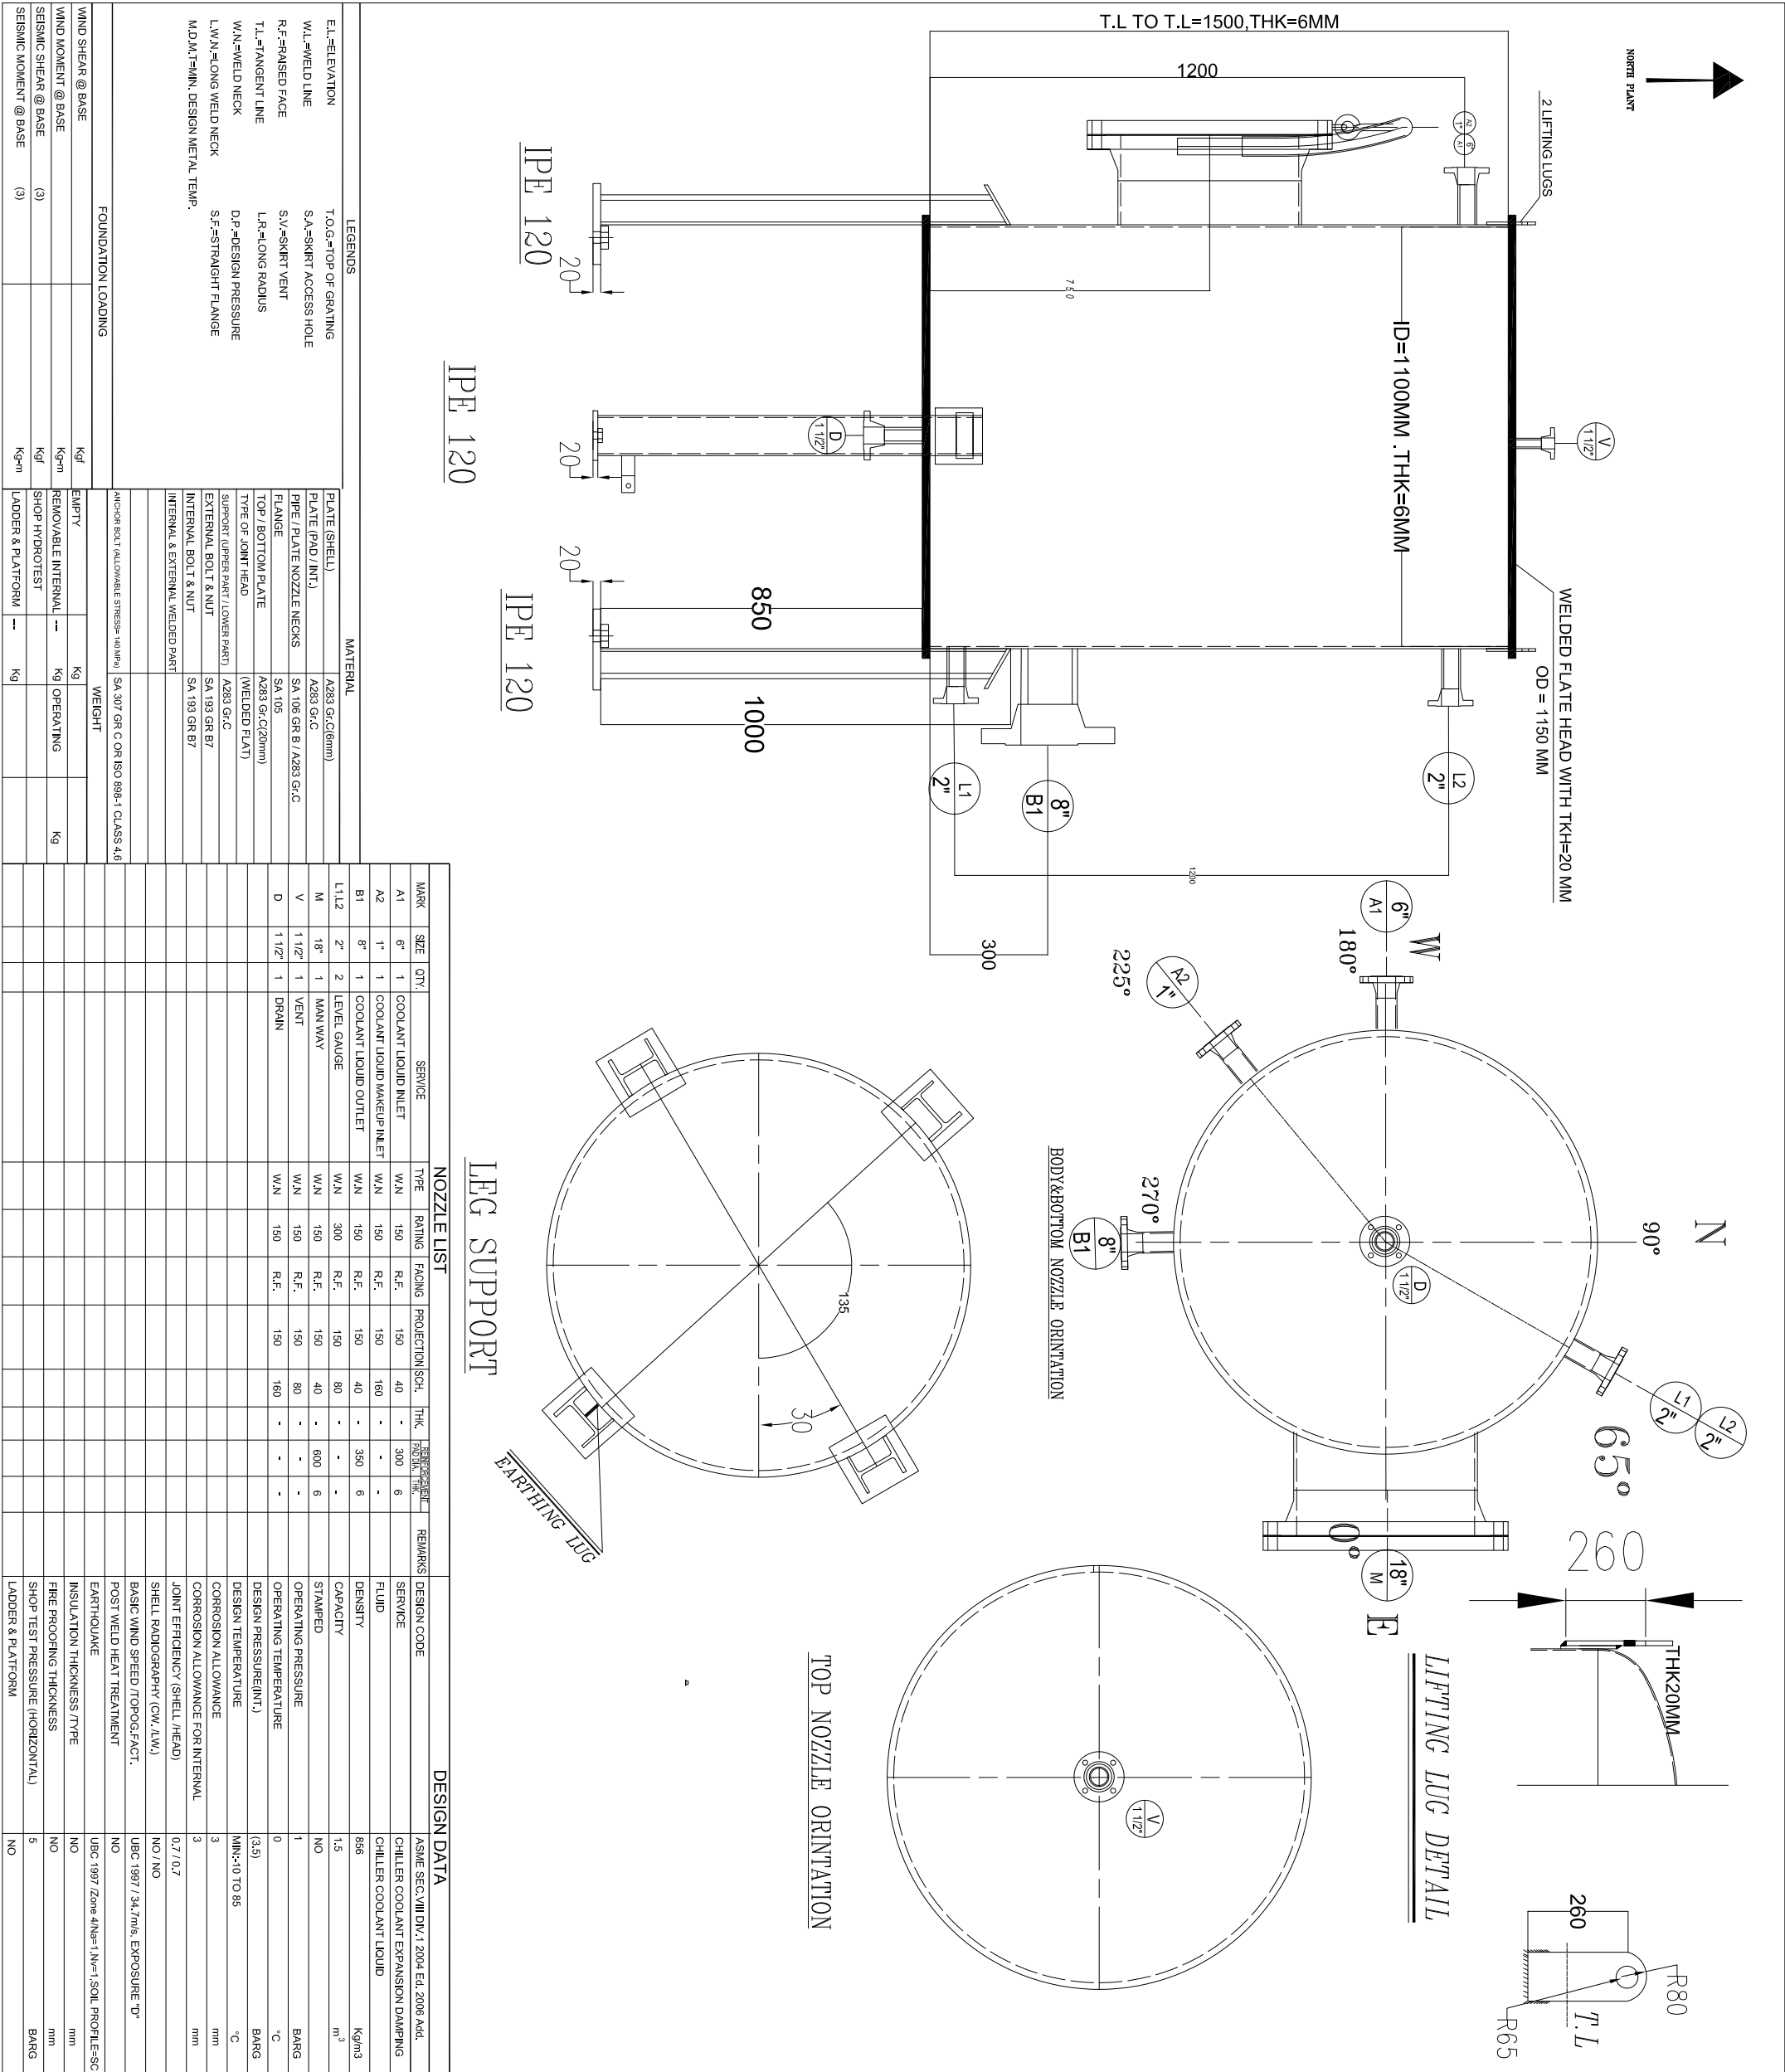

NOTES:

(1) ALL DIMENSIONS ARE IN MILLIMETERS UNLESS OTHERWISE NOTED.

00	ISSUED FOR APPROVAL	A.P.K	R.M	SH.H	08/14/2024	
REV.	DESCRIPTION	PRPD	CHK	APP	DATE	
CLIENT: AFTAB OIL REFINING CO.						
PROJECT : ISO RECYCLE DEWAXING UNIT(DWU)						
CONTRACTOR : AFTAB OIL REFINING CO.						
TITLE: CHILLER EXPANSION DRUM (D-5103)						
CLIENT DRAWING NUMBER: *****						
ATM-DWU-EN-MEC-DWG-0001						
CONTRACTOR DWG NO. : *****		SCALE:	SIZE: A3			
*****		SHEET 01 OF 01	REV.: 00			